


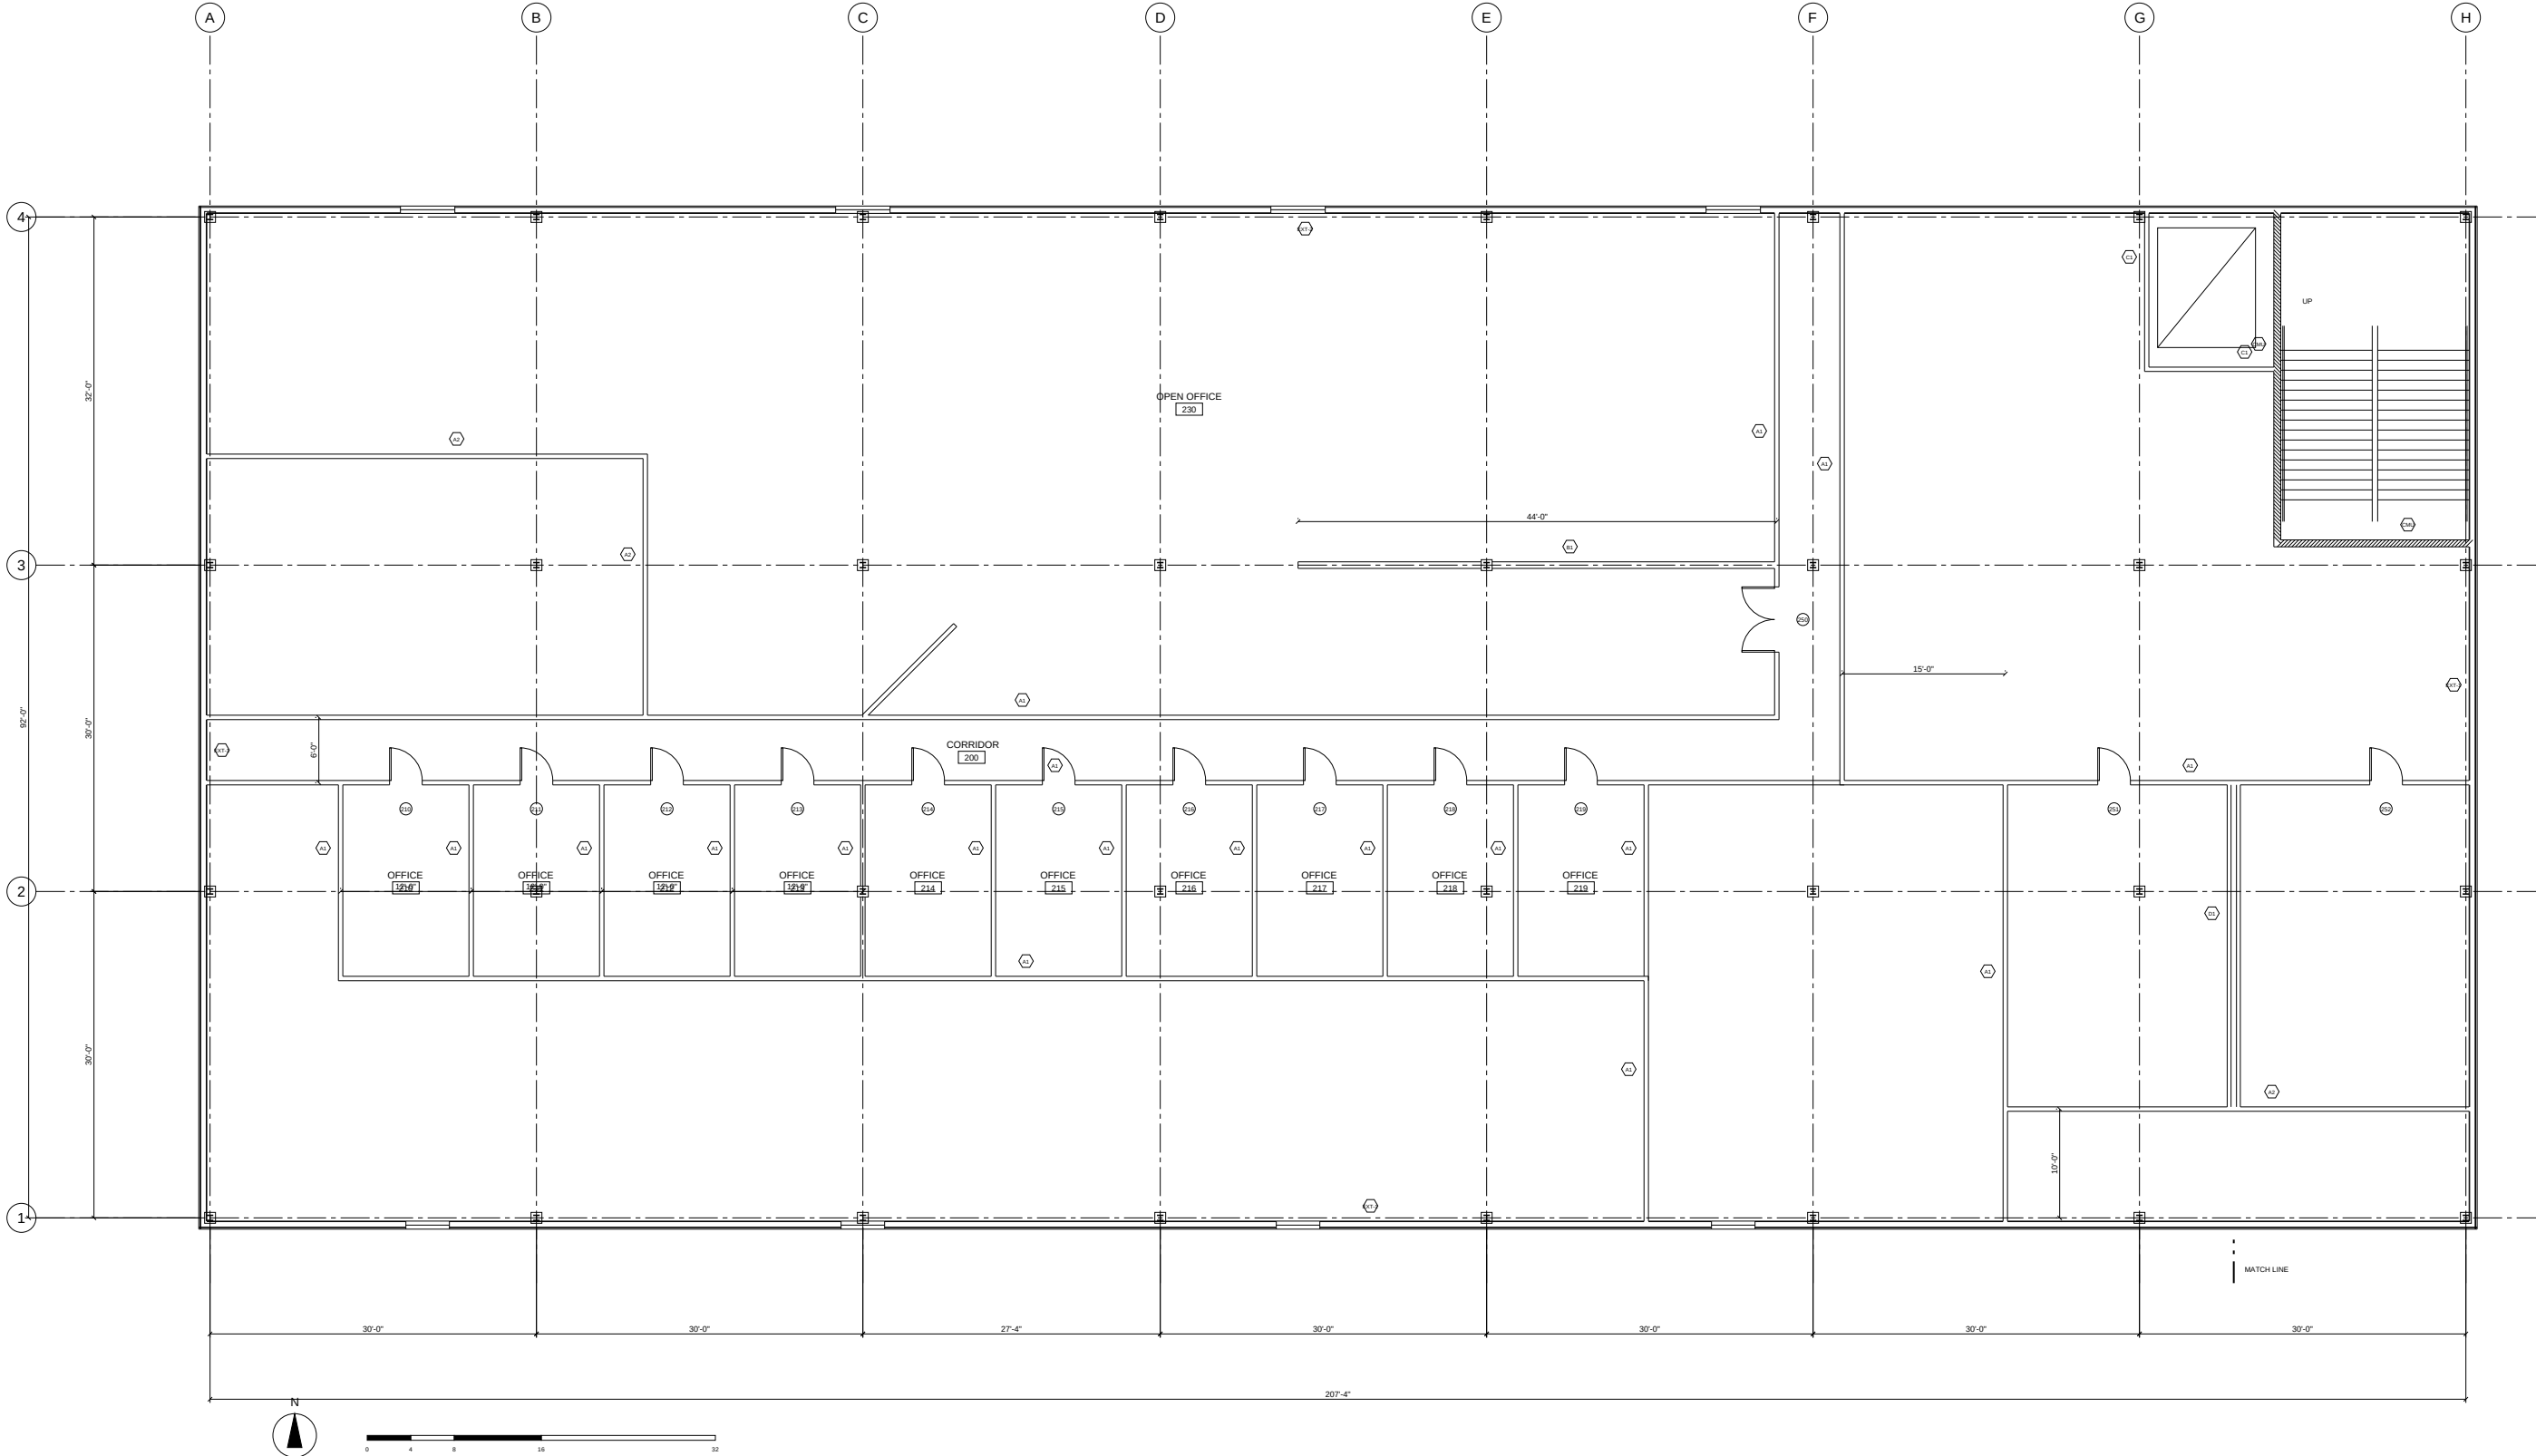

- GENERAL NOTES
1. ALL PARTITIONS TYPE A3 U.N.O.
 2. SEE A-501 FOR PARTITION TYPES
 3. SEE A-601 FOR DOOR SCHEDULE
 4. DIMENSIONS ARE TO FACE OF STUD OR GRID U.N.O.
 5. DO NOT SCALE DRAWINGS
 6. PROVIDE BLOCKING AT ALL WALL-MOUNTED EQUIPMENT
- KEYNOTES
- 08 41 13 ALUMINUM STOREFRONT
 - 09 21 16 GYPSUM BOARD ASSEMBLY
 - 09 22 15 NON-STRUCT. METAL FRAMING
 - 04 22 00 CMU - BY OTHERS

1 LEVEL 2 FLOOR PLAN
SCALE: 1/8" = 1'-0"