




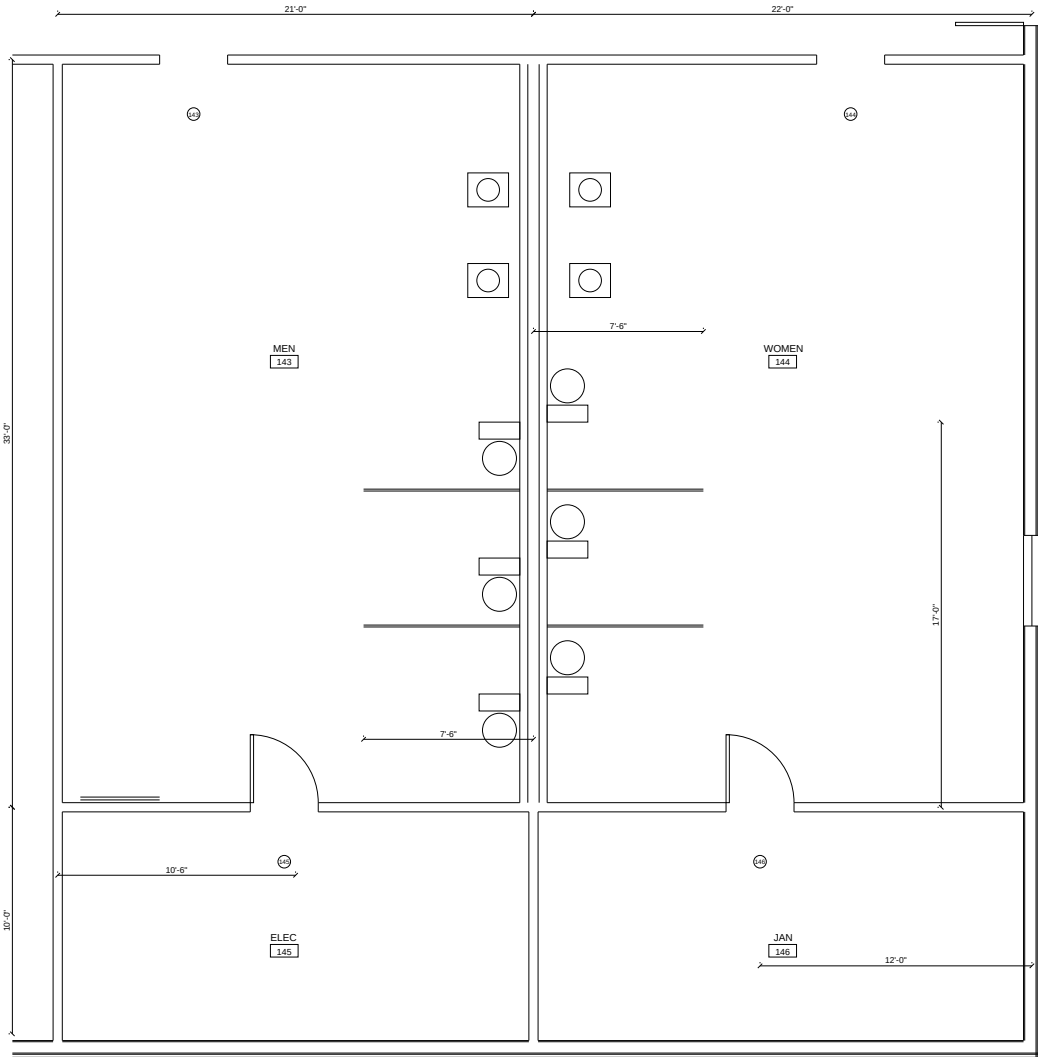

1 ENLARGED RESTROOM PLAN
SCALE: 1/4" = 1'-0"

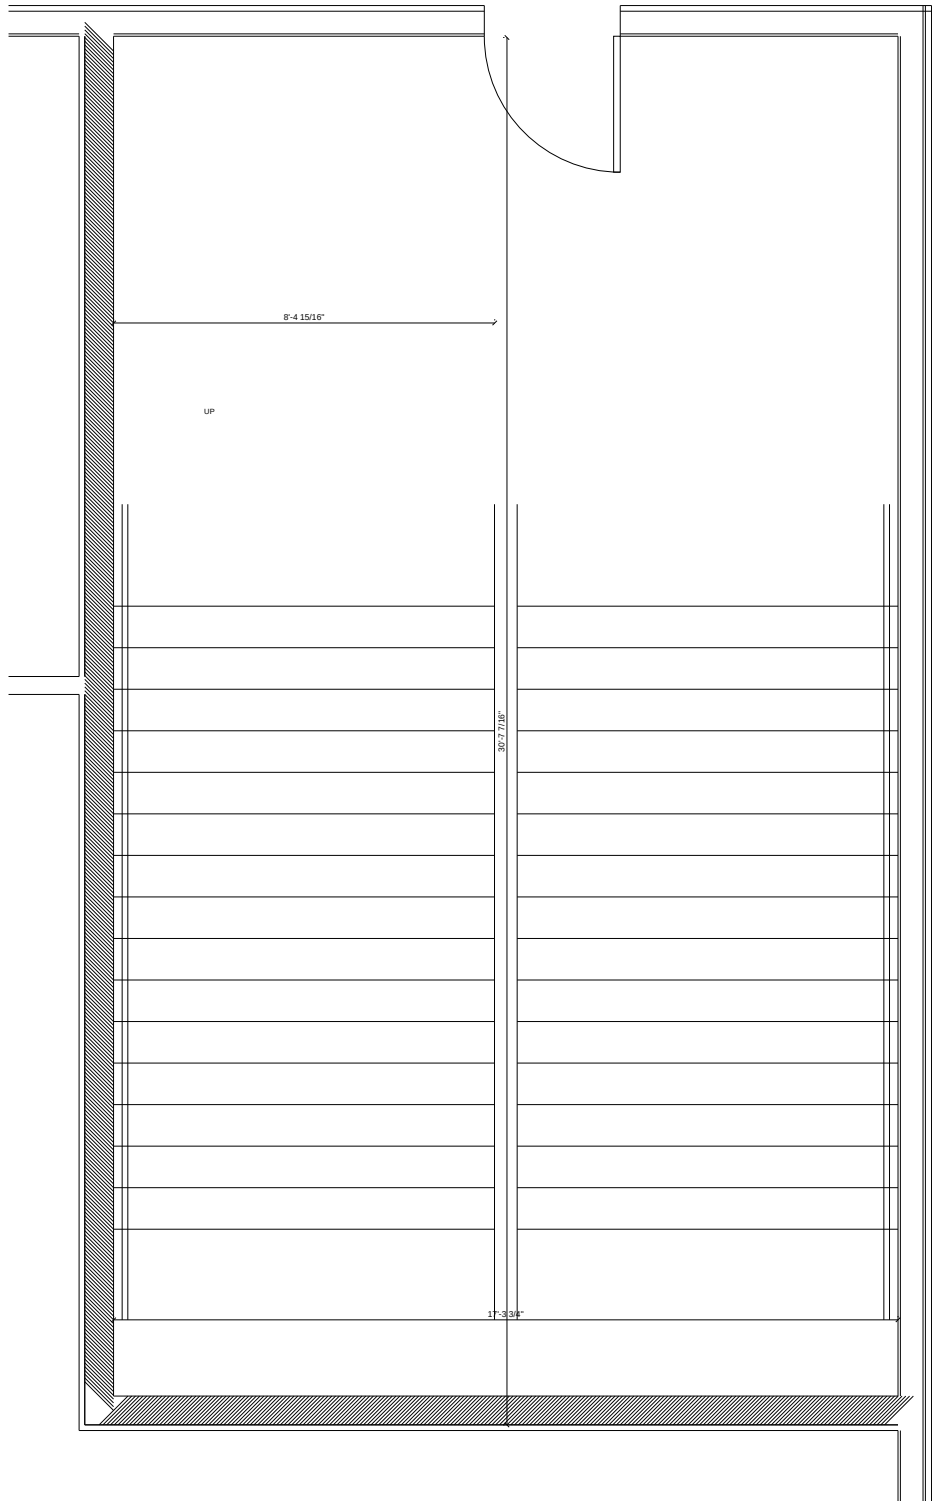

1 ENLARGED STAIR PLAN
SCALE: 1/2" = 1'-0"

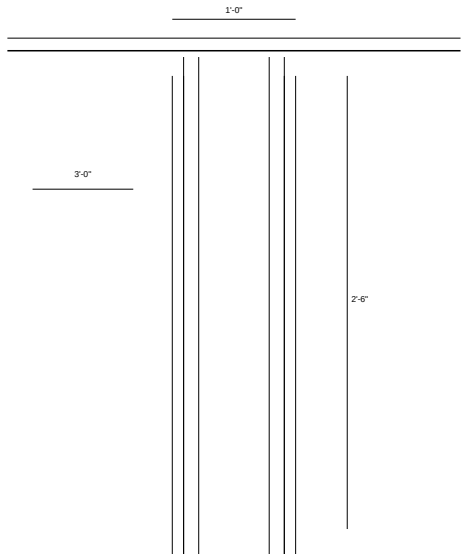

1 HEAD OF WALL DETAIL
SCALE: NTS

REVISIONS

DATE: 08/04/2025
ISSUE: BID SET

SCALE: AS NOTED

ENLARGED PLANS

A-401