


GENERAL NOTES
1. ALL PARTITIONS TYPE A1 U.N.O.
2. SEE A-501 FOR PARTITION TYPES
3. SEE A-601 FOR DOOR SCHEDULE
4. DIMENSIONS ARE TO FACE OF STUD OR GRID U.N.O.
5. DO NOT SCALE DRAWINGS
6. PROVIDE BLOCKING AT ALL WALL-MOUNTED EQUIPMENT
KEYNOTES
08 41 13 ALUMINUM STOREFRONT
09 21 16 GYPSUM BOARD ASSEMBLY
09 22 16 NON-STRUCT. METAL FRAMING
04 22 00 CMU - BY OTHERS

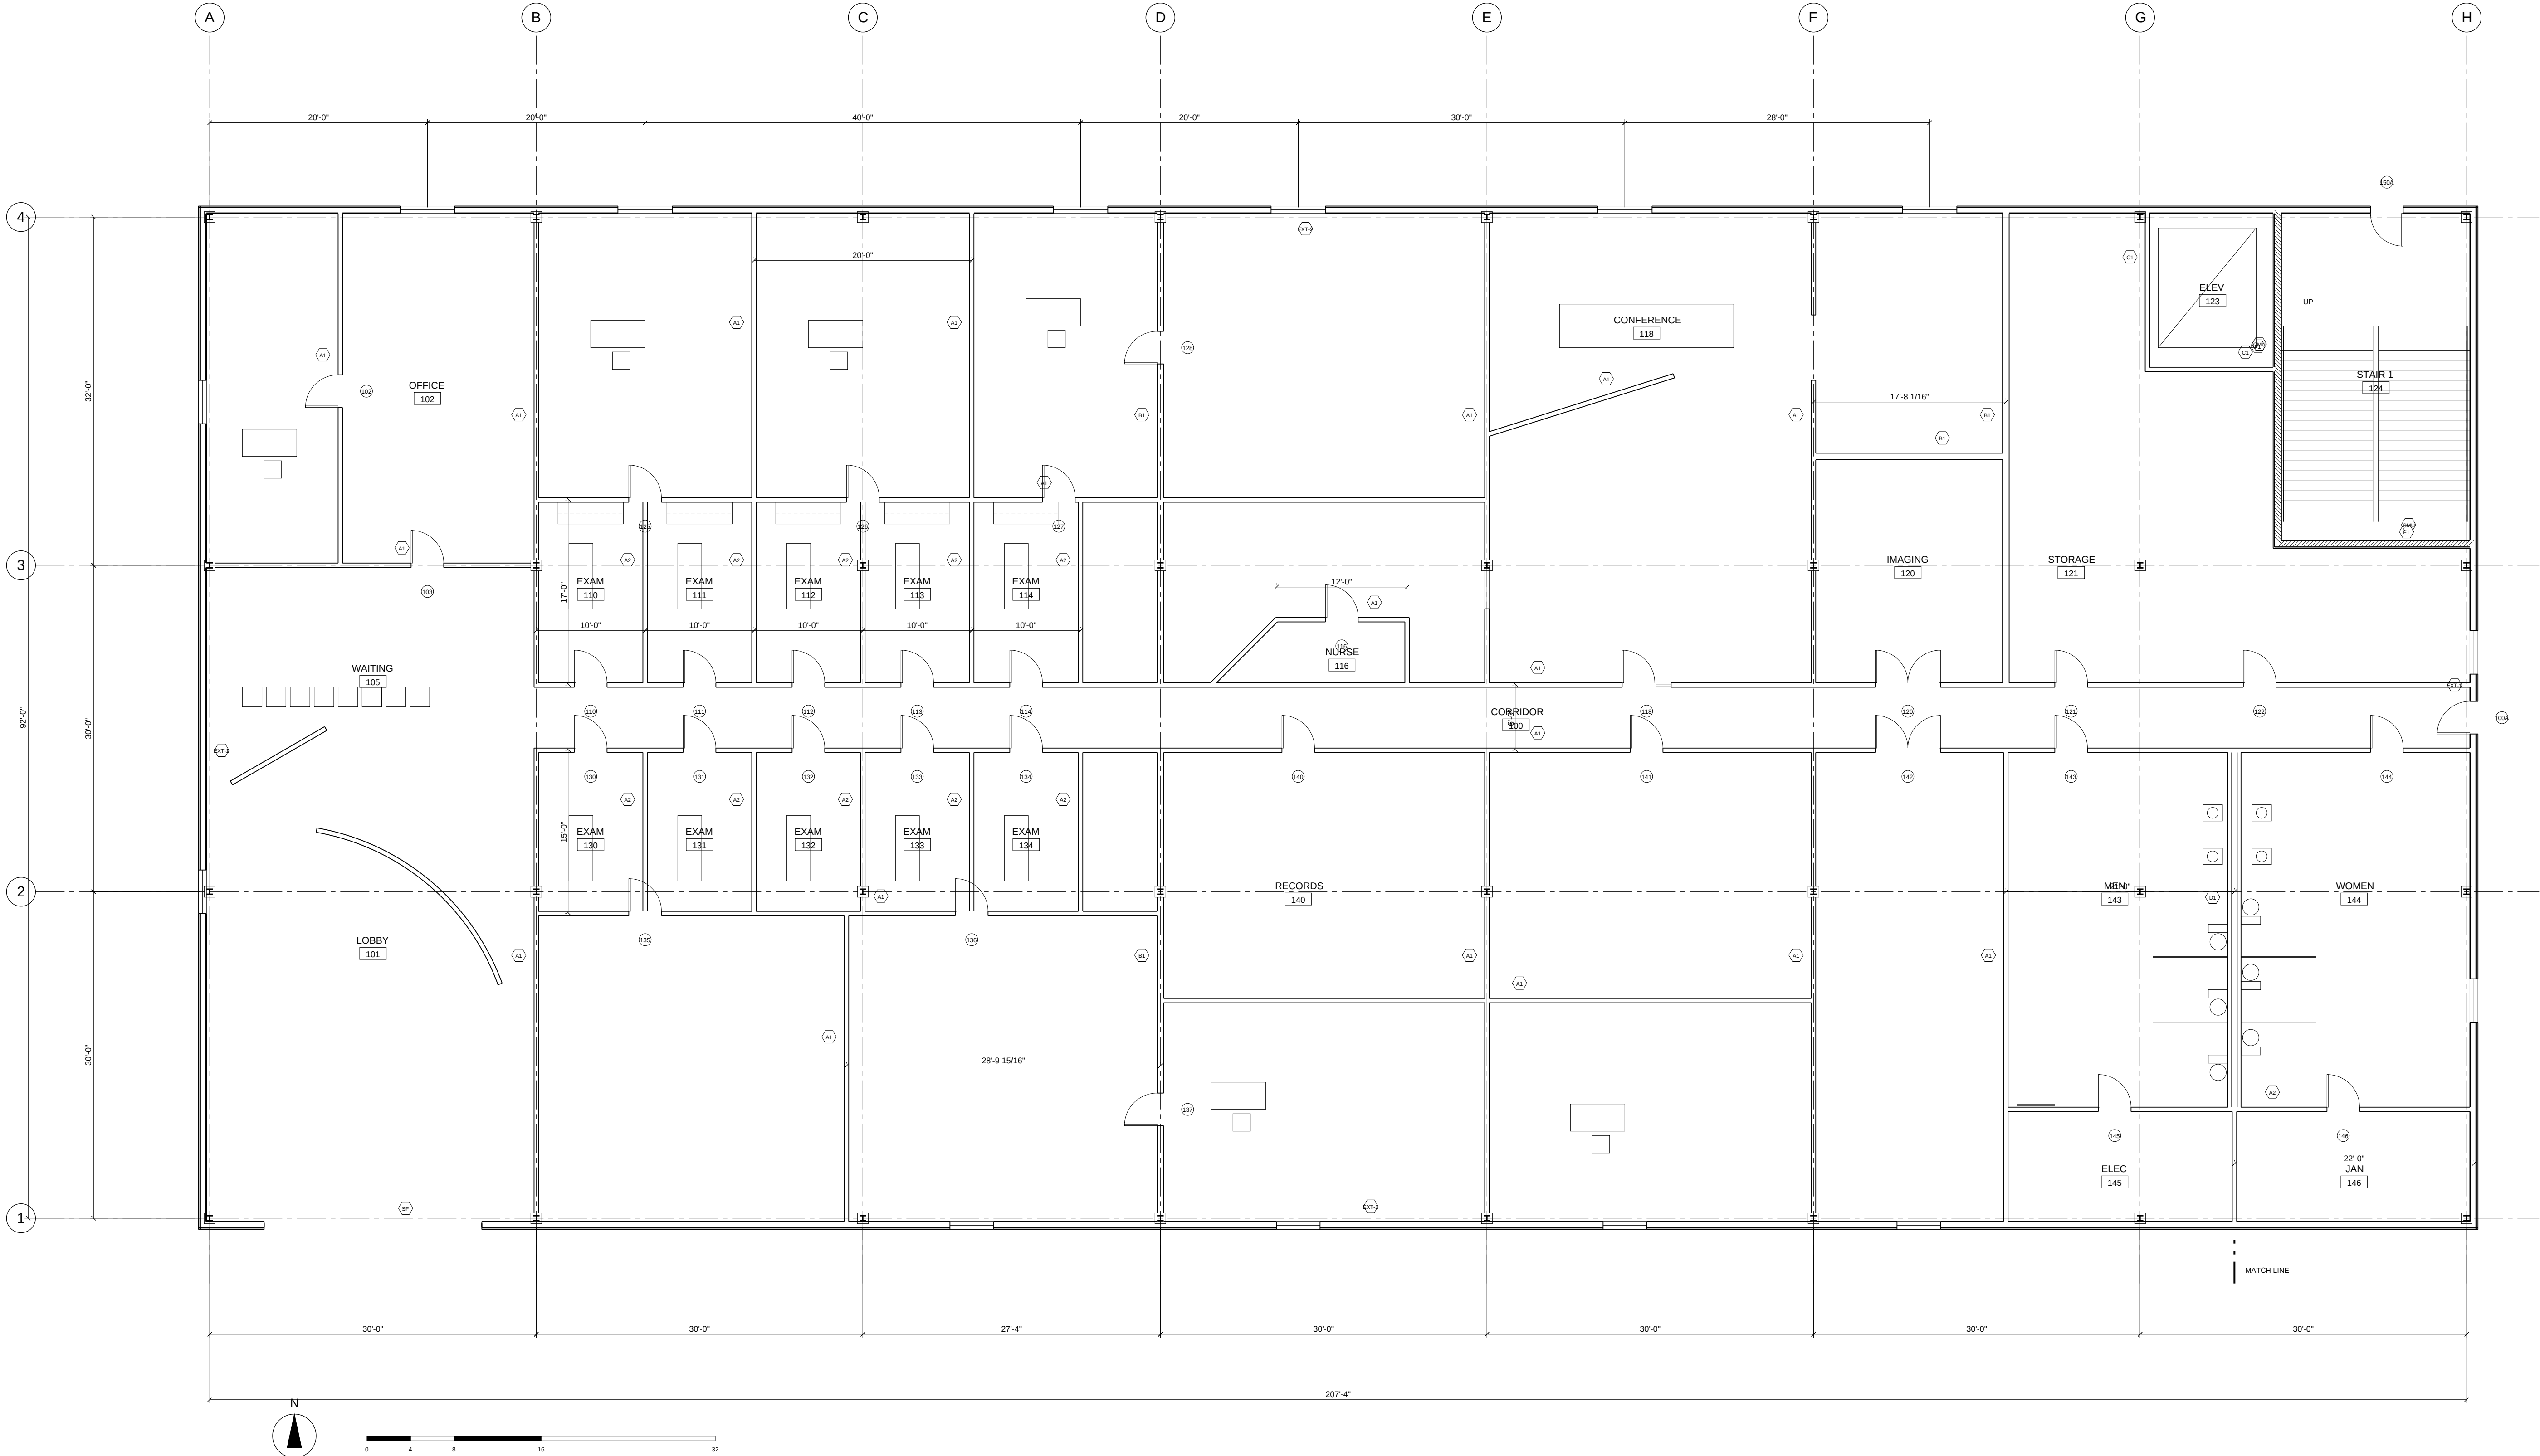

1 LEVEL 1 FLOOR PLAN
SCALE: 1/8" = 1'-0"

REVISIONS
1 08/04/2026 BID SET

DATE: 08/04/2026
ISSUE: BID SET

SCALE: 1/8" = 1'-0"

LEVEL 1 FLOOR PLAN

A-101