


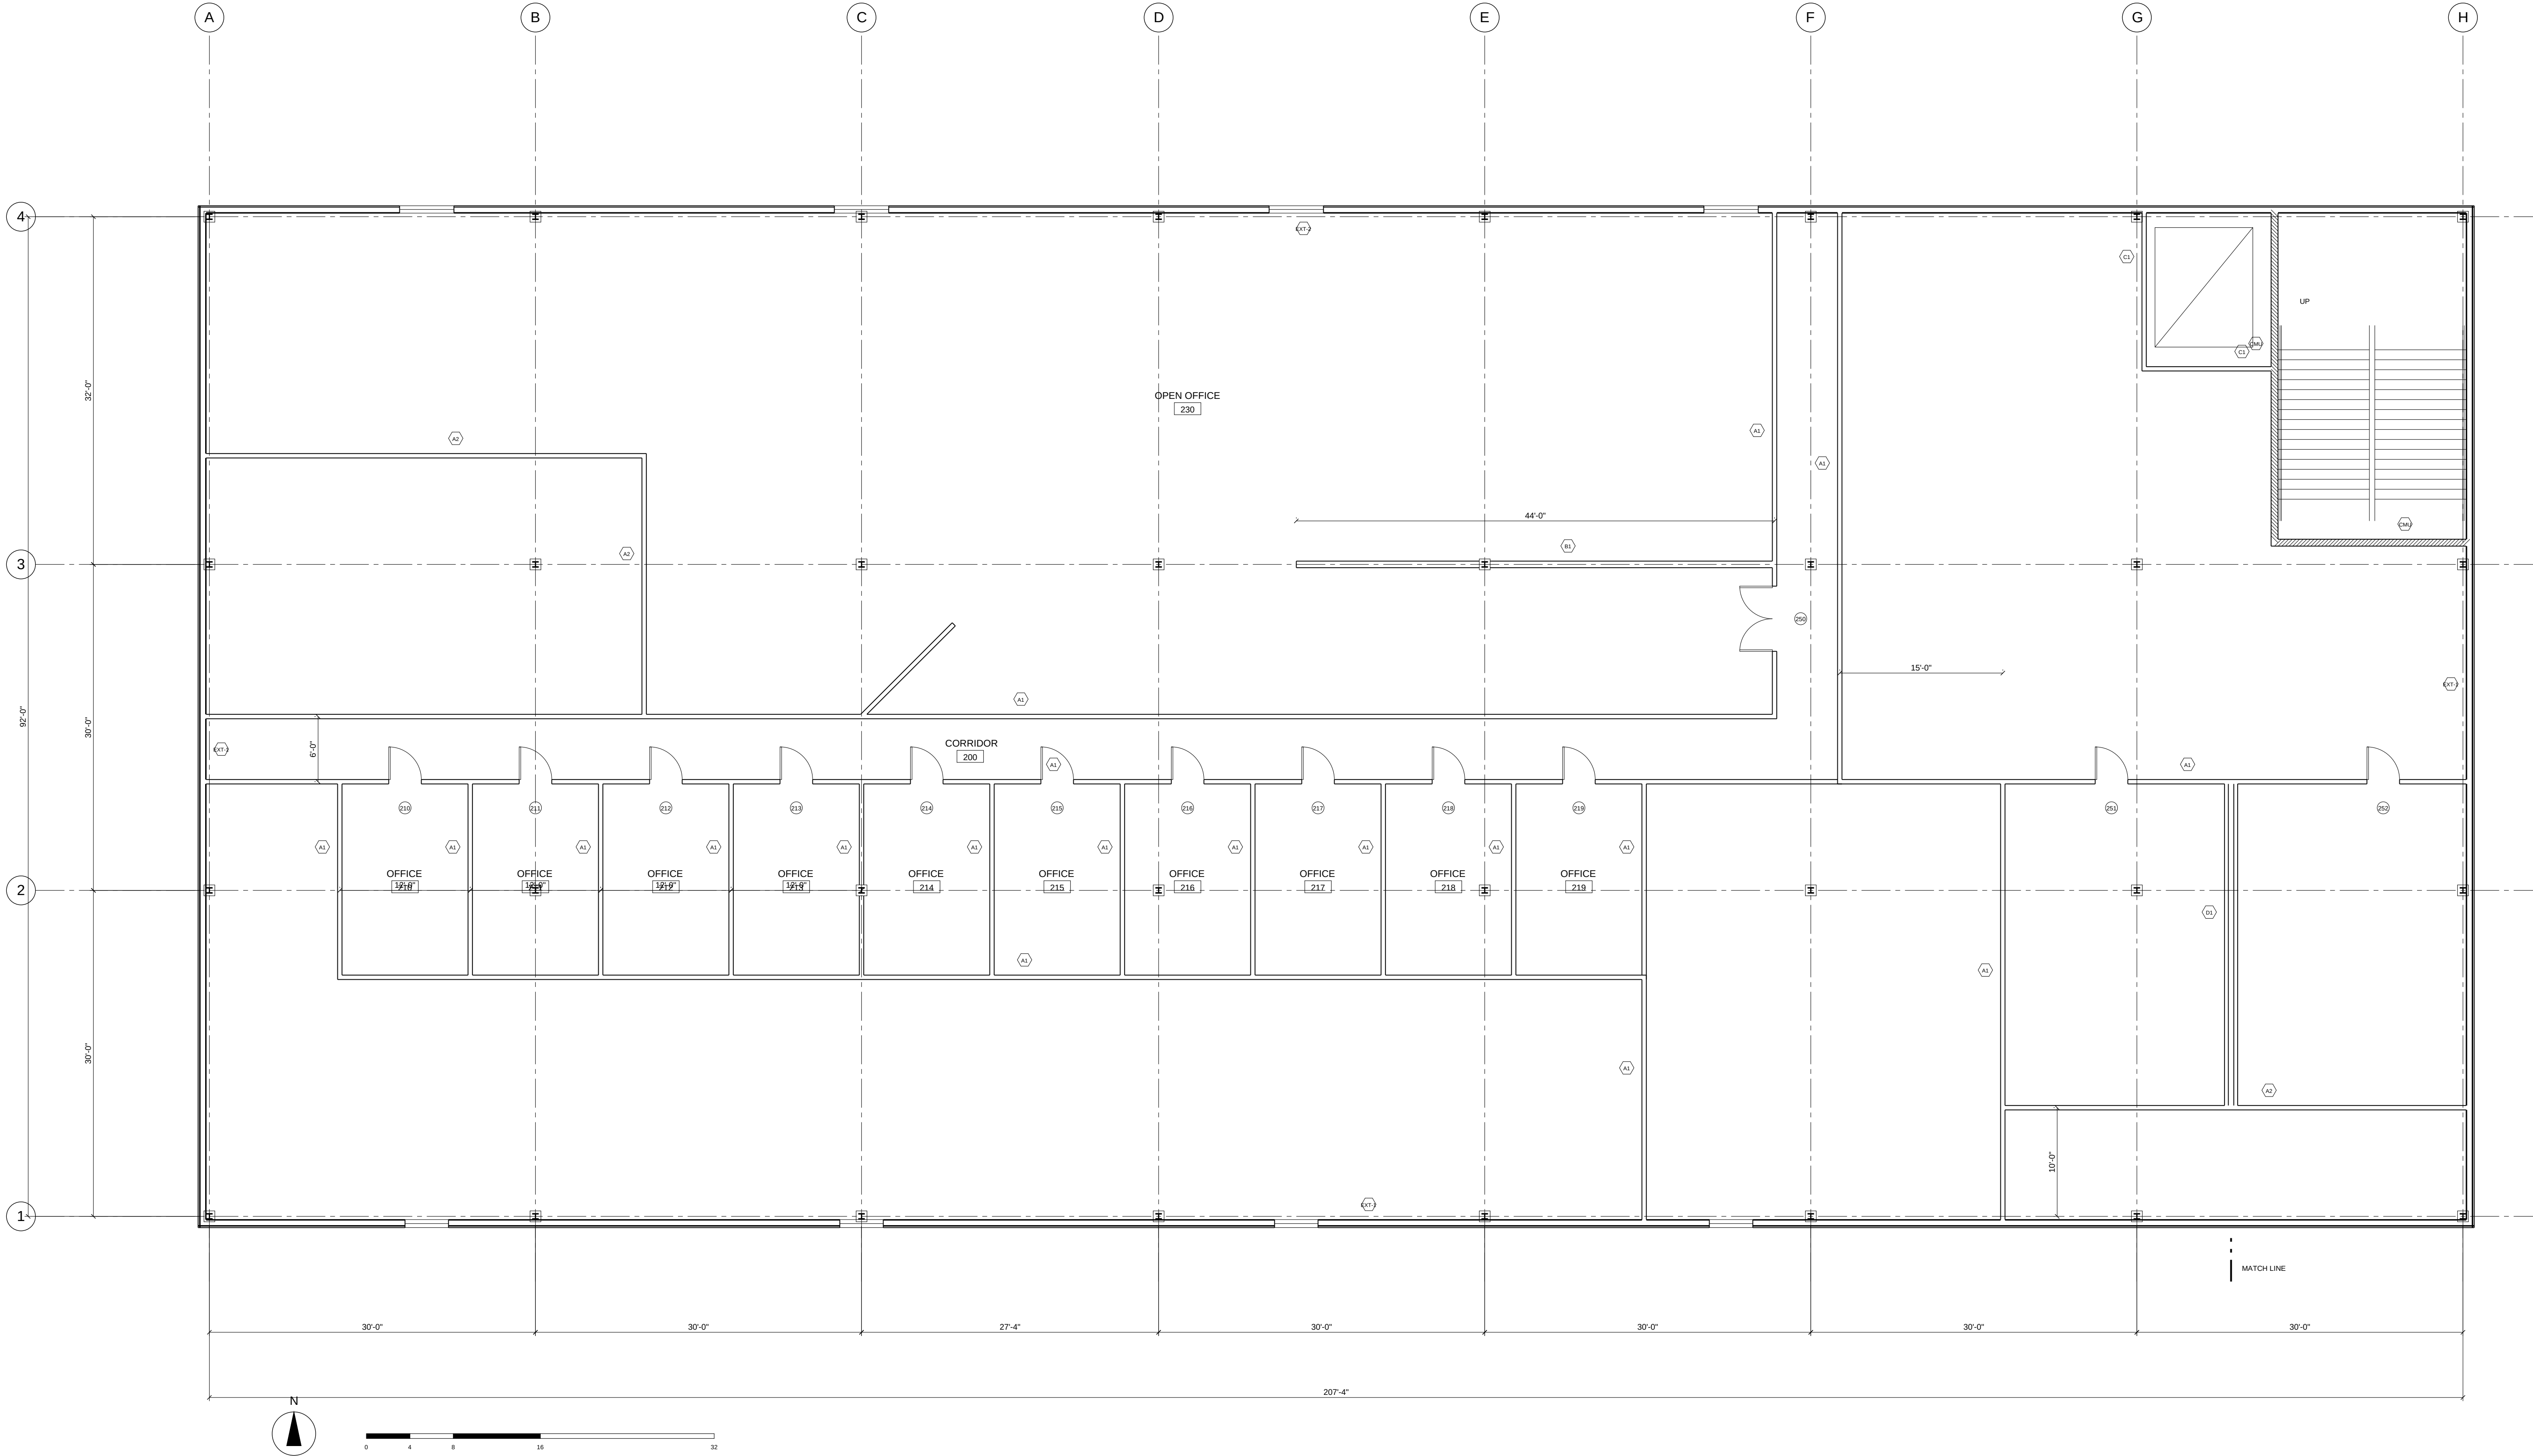

GENERAL NOTES
1. ALL PARTITIONS TYPE A3 U.N.O.
2. SEE A-501 FOR PARTITION TYPES
3. SEE A-601 FOR DOOR SCHEDULE
4. DIMENSIONS ARE TO FACE OF STUD OR GRID U.N.O.
5. DO NOT SCALE DRAWINGS
6. PROVIDE BLOCKING AT ALL WALL-MOUNTED EQUIPMENT
KEYNOTES
08 41 13 ALUMINUM STOREFRONT
09 21 16 GYPSUM BOARD ASSEMBLY
09 22 16 NON-STRUCT. METAL FRAMING
04 22 00 CMU - BY OTHERS

ARCADIA DESIGN COLLECTIVE
SYNTHETIC TEST SET - NOT A REAL PROJECT
1200 E CAMELBACK RD, PHOENIX AZ

MESA RIDGE MEDICAL
OFFICE BUILDING
4410 S RIDGE PKWY, PHOENIX AZ
PROJECT NO. 25-118

REVISIONS
1 08/04/2026 BID SET

DATE: 08/04/2026
ISSUE: BID SET

SCALE: 1/8" = 1'-0"

LEVEL 2 FLOOR PLAN

A-102