
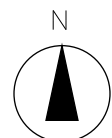


- GENERAL NOTES
1. ALL PARTITIONS TYPE A1 U.N.D.
 2. SEE A-501 FOR PARTITION TYPES
 3. SEE A-601 FOR DOOR SCHEDULE
 4. DIMENSIONS ARE TO FACE OF STUD OR GRID U.N.D.
 5. DO NOT SCALE DRAWINGS
 6. PROVIDE BLOCKING AT ALL WALL-MOUNTED EQUIPMENT
- KEYNOTES
- 08-41-13 ALUMINUM STOREFRONT
09-21-16 GYPSUM BOARD ASSEMBLY
09-22-16 NON-STRUCT. METAL FRAMING
04-22-00 CMU - BY OTHERS

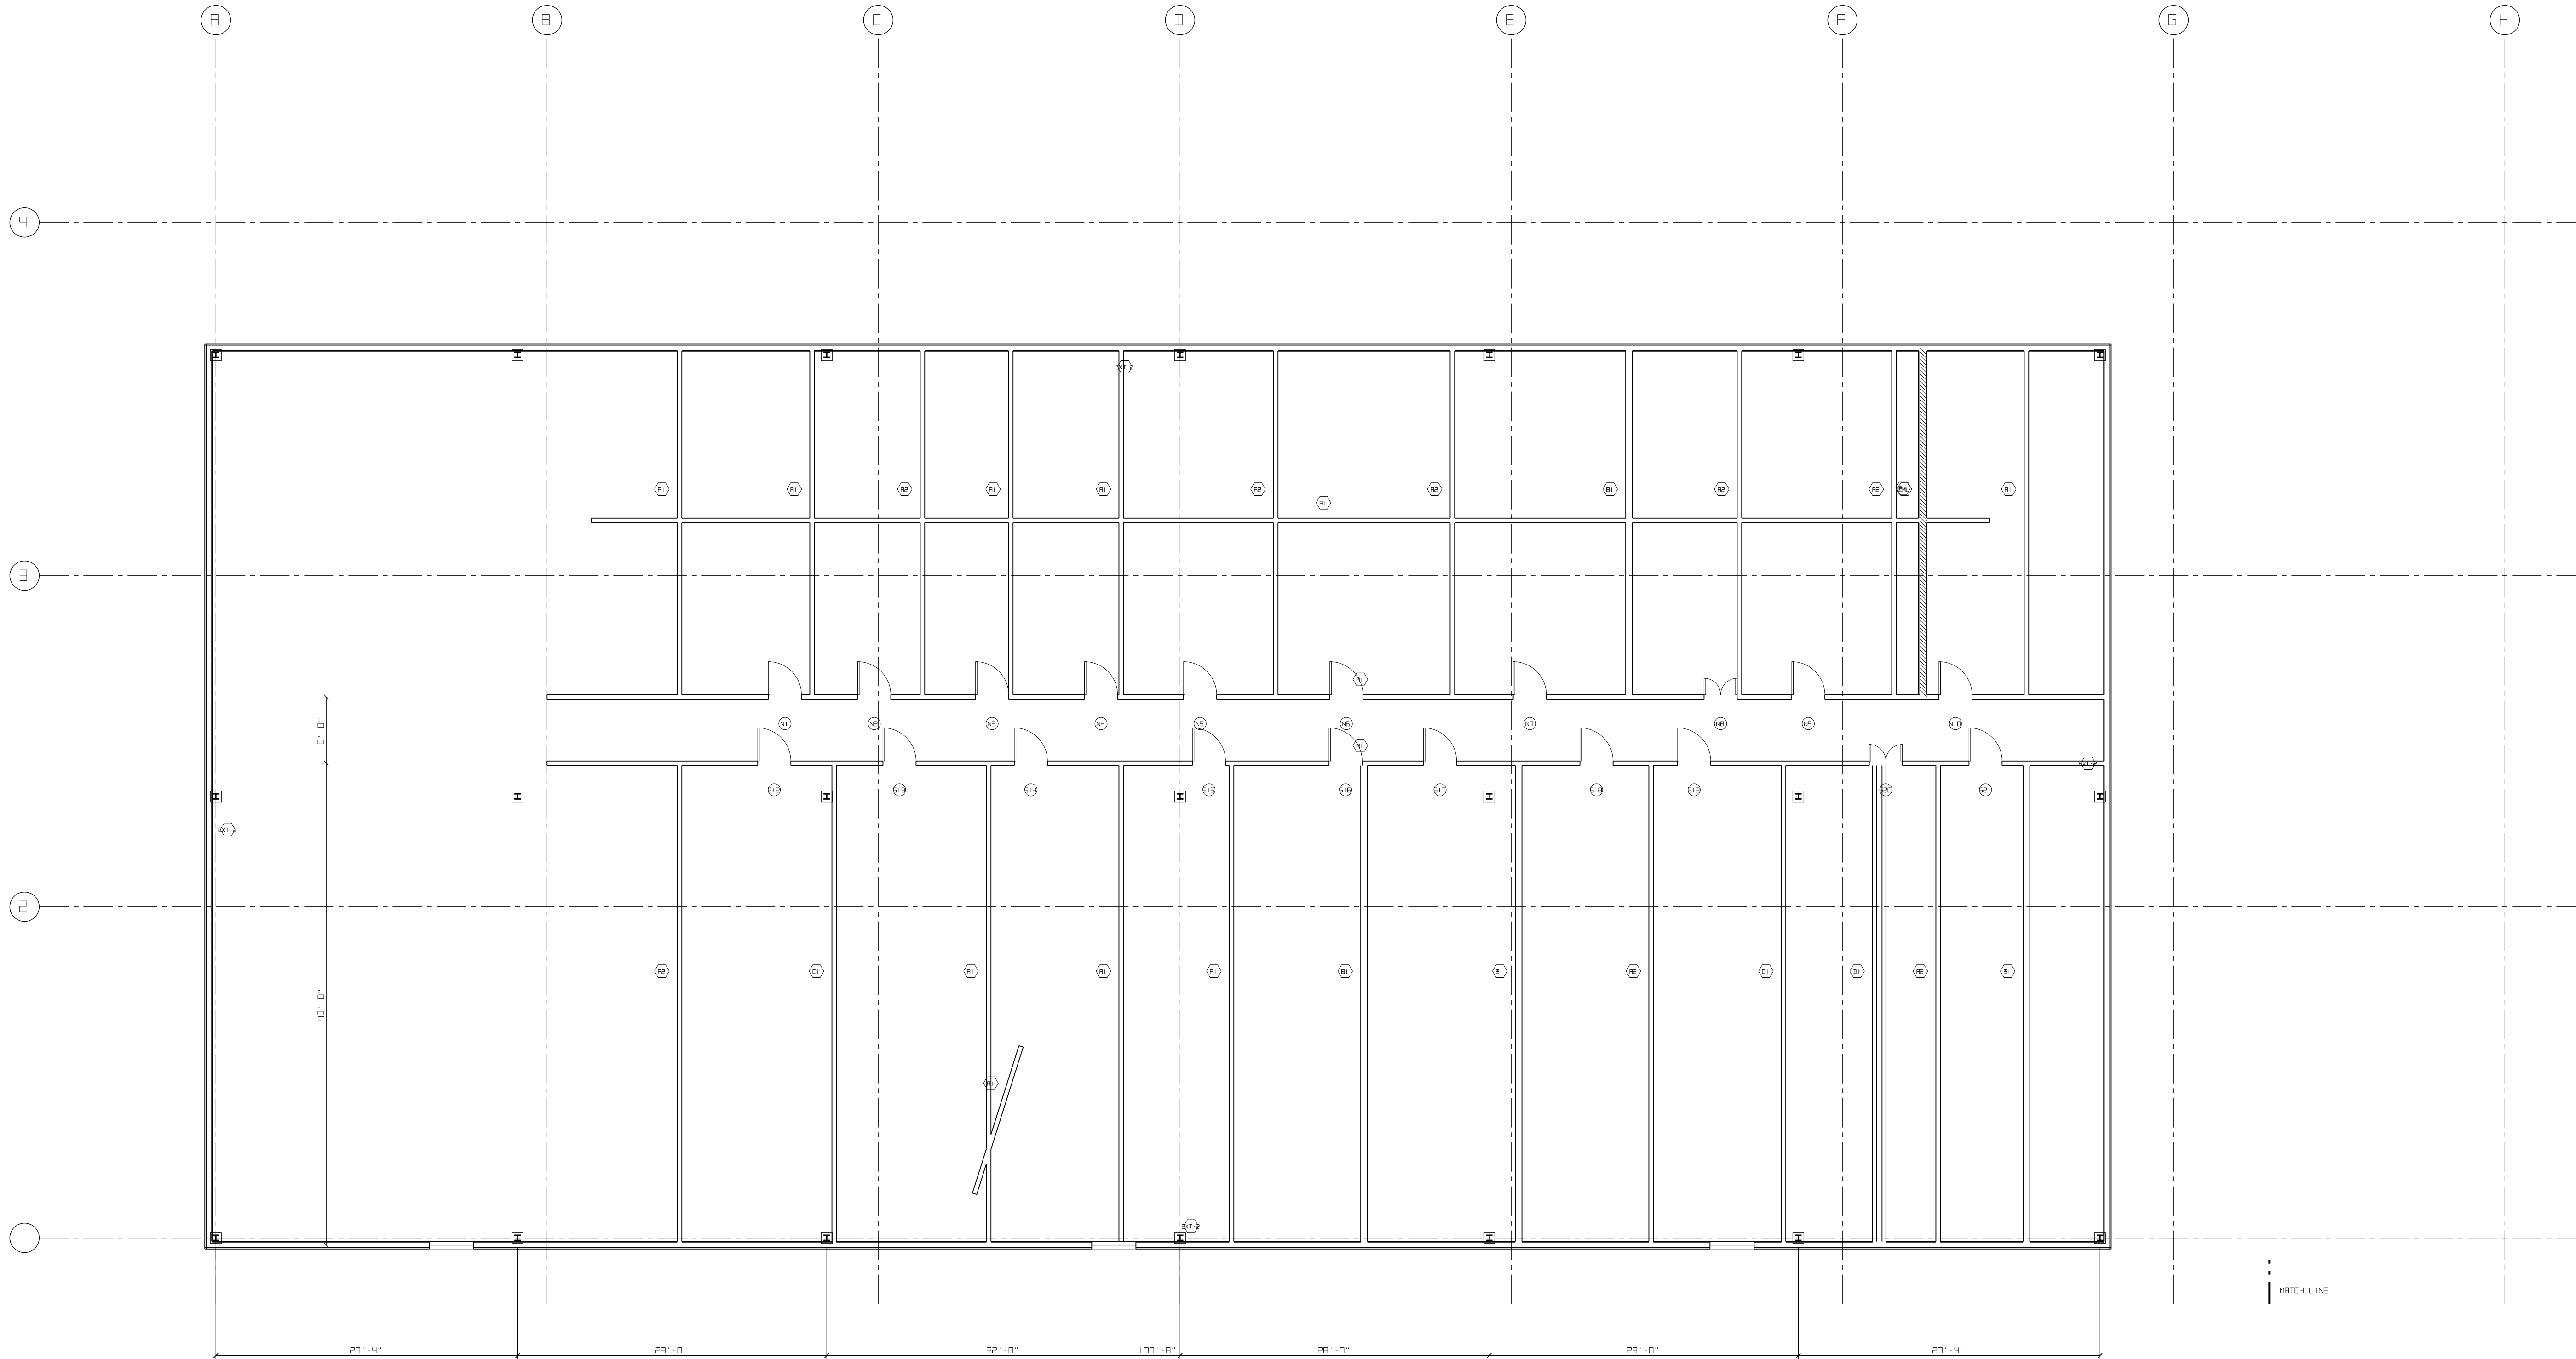

1 LEVEL 1 FLOOR PLAN
SCALE: 1/8" = 1'-0"

REVISIONS
1 08/24/2025 013 SET

DATE: 08/04/2025
ISSUE: 013 SET

SCALE: 1/8" = 1'-0"

HOLDOUT 111875

H-111875